
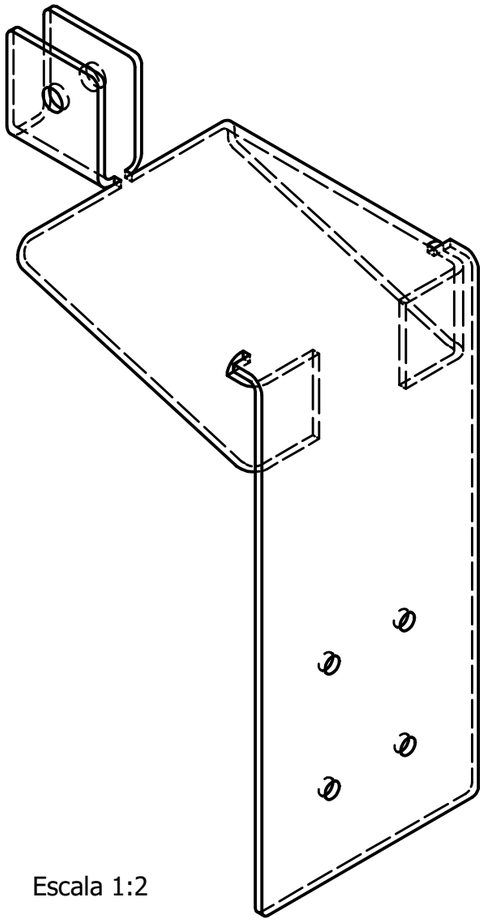



Escala 1:2

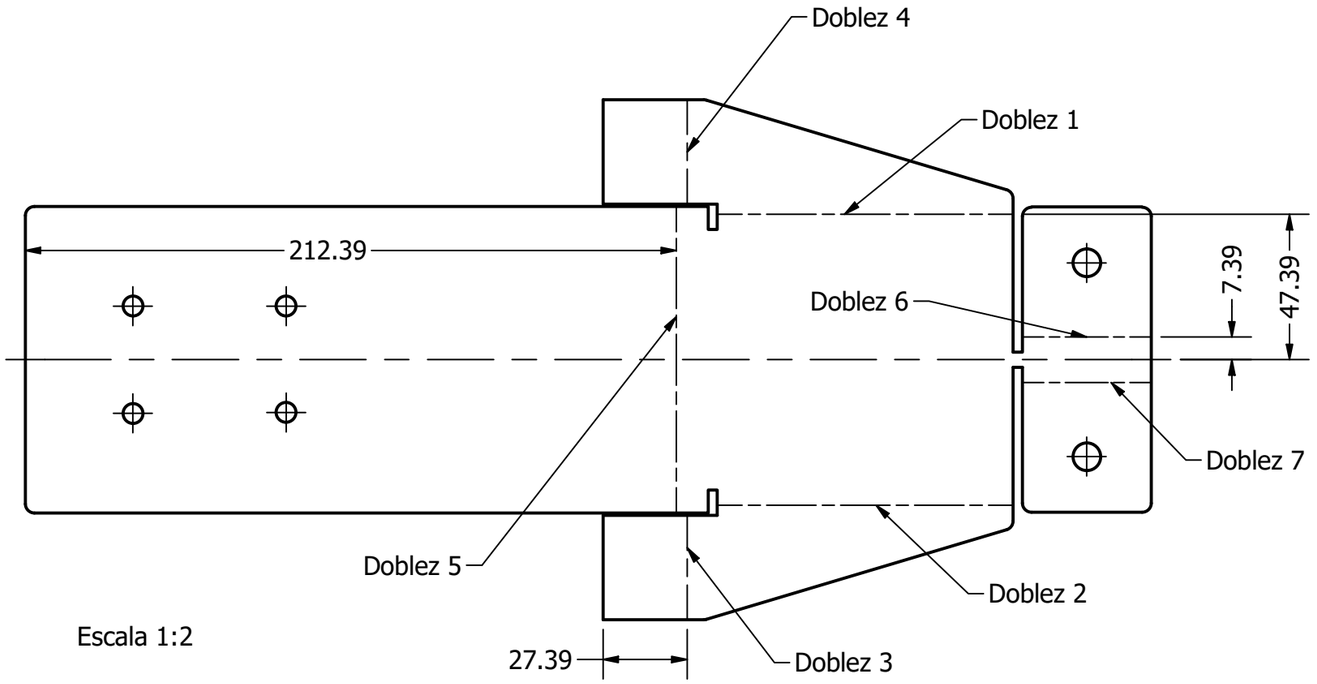


Escala 1:2

NOTAS:

1. Todos los dobleces indicados en el plano son a 90°.
2. El proceso de plegado debe realizarse respetando el orden de la enumeración indicada.
3. Los dobleces identificados del 1 al 5 corresponden a dobleces internos.
4. Los dobleces identificados del 6 al 7 corresponden a dobleces externos.
5. El radio interno de doblez para los plegados será de 3 mm.
6. Todas las dimensiones indicadas en el plano están expresadas en milímetros (mm).

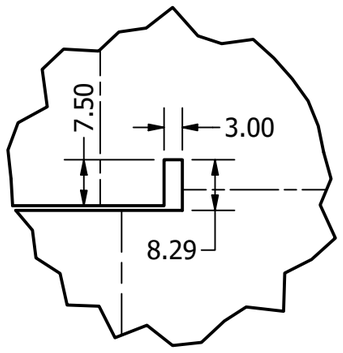

Detalle A
Escala 1 : 1

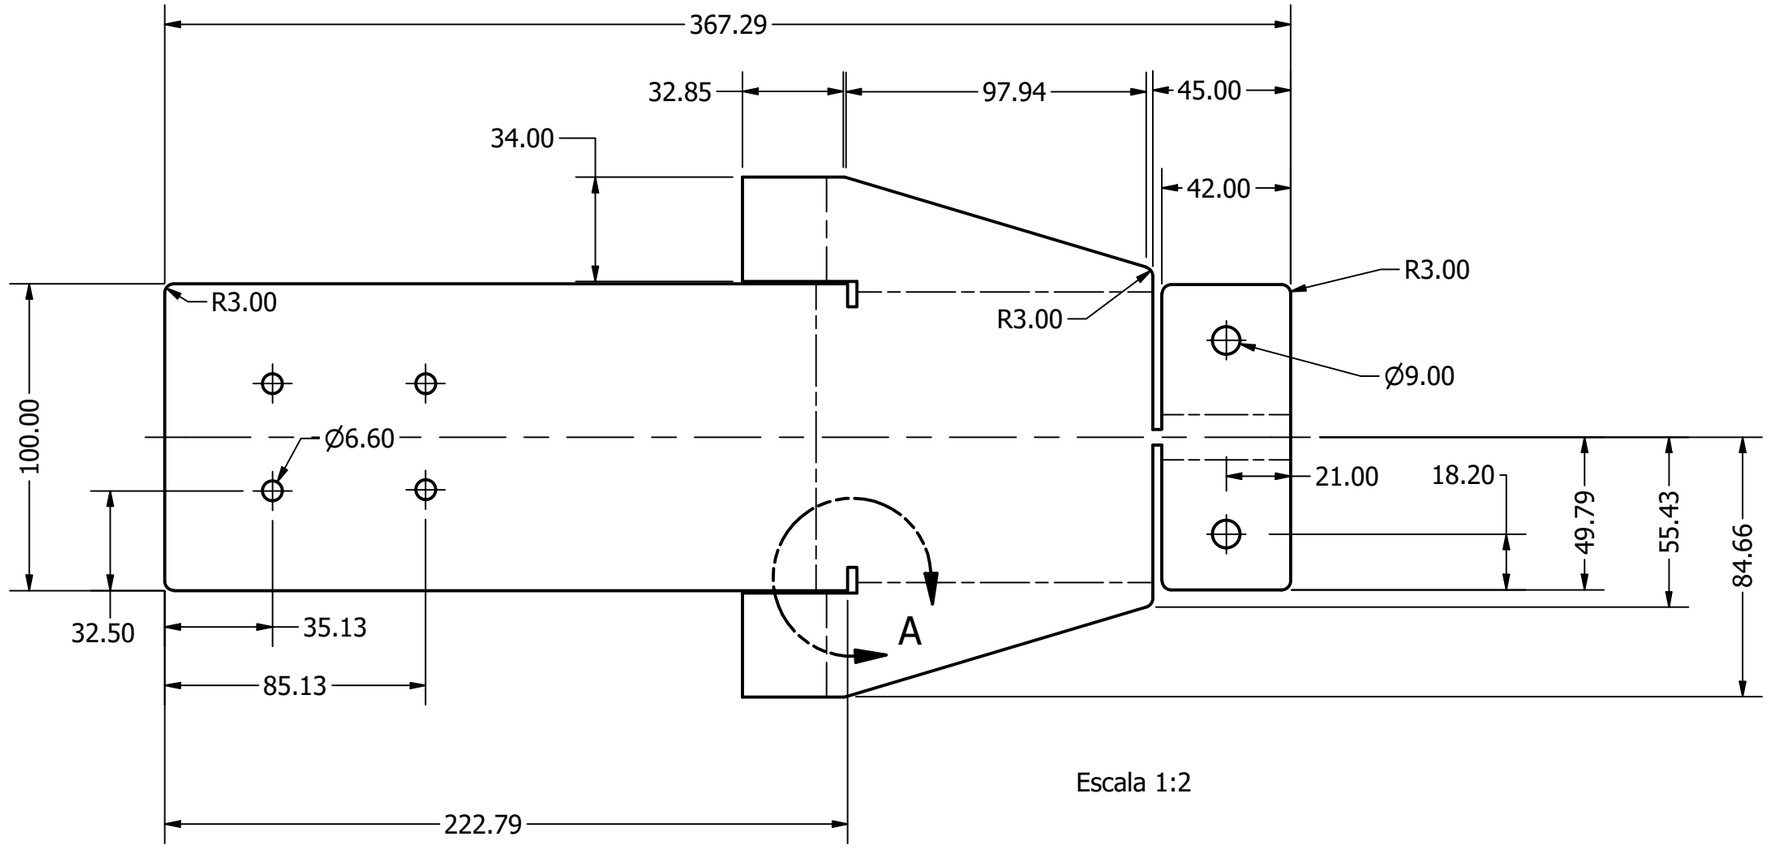

Escala 1:2